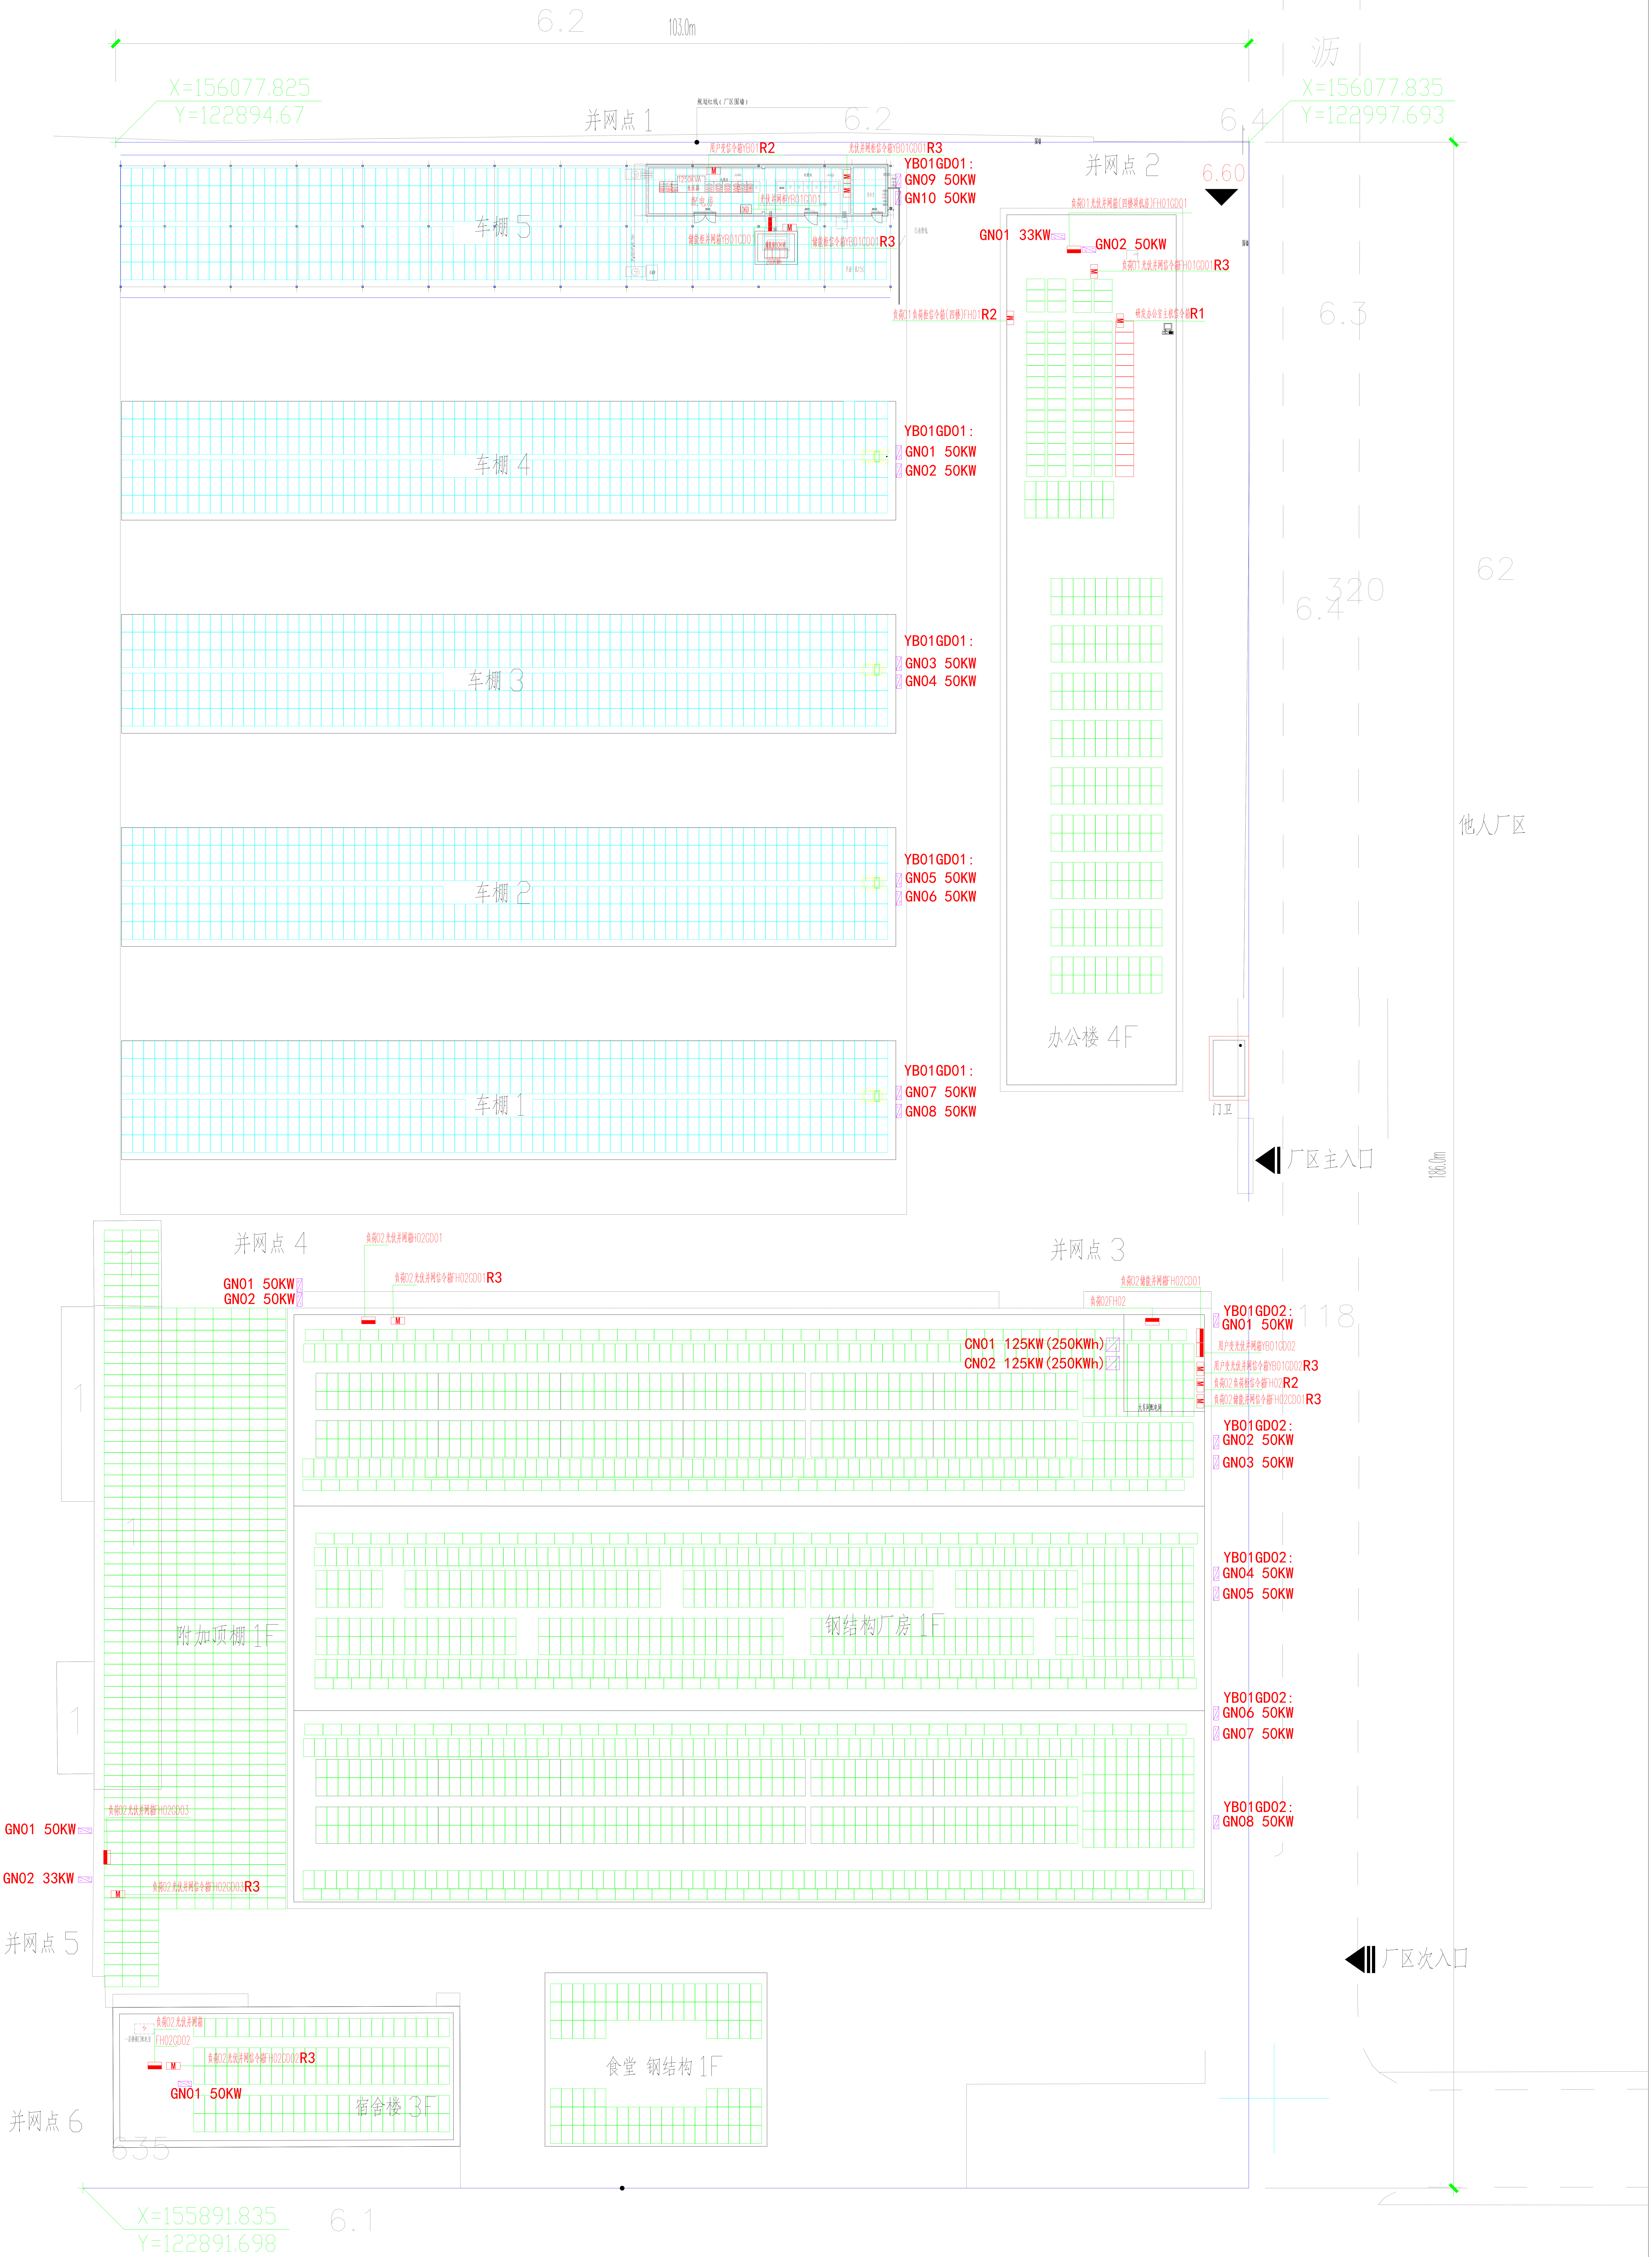
6.2
103.0m
X=156077.825
Y=122894.67
并网点 1
规划红线（厂区围墙）
6.2
6.4
沥
X=156077.835
Y=122997.693
用户变信令箱YB01R2
光伏并网柜信令箱YB01GD01R3
YB01GD01:
GN09 50KW
GN10 50KW
1250KVA
变压器
配电房
光伏并网柜YB01GD01
储能柜并网箱YB01CD01
储能柜信令箱YB01CD01R3
储能柜80KW
200KWh
已有管线
车棚 5
并网点 2
6.60
负荷01光伏并网箱(四楼顶机房)FH01GD01
GN01 33KW
GN02 50KW
负荷01光伏并网信令箱FH01GD01R3
负荷01负荷柜信令箱(四楼)FH01R2
研发办公室主机信令箱R1
6.3
车棚 4
YB01GD01:
GN01 50KW
GN02 50KW
62
6.4
320
车棚 3
YB01GD01:
GN03 50KW
GN04 50KW
他人厂区
车棚 2
YB01GD01:
GN05 50KW
GN06 50KW
办公楼 4F
车棚 1
YB01GD01:
GN07 50KW
GN08 50KW
门卫
厂区主入口
186.0m
并网点 4
负荷02光伏并网箱H02GD01
负荷02光伏并网信令箱FH02GD01R3
GN01 50KW
GN02 50KW
并网点 3
负荷02储能并网箱FH02CD01
负荷02FH02
CN01 125KW(250KWh)
CN02 125KW(250KWh)
YB01GD02:
GN01 50KW
118
用户变光伏并网箱YB01GD02
用户变光伏并网信令箱YB01GD02R3
负荷02负荷柜信令箱FH02R2
负荷02储能并网信令箱FH02CD01R3
大车间配电间
YB01GD02:
GN02 50KW
GN03 50KW
1
1
1
1
附加顶棚 1F
钢结构厂房 1F
YB01GD02:
GN04 50KW
GN05 50KW
YB01GD02:
GN06 50KW
GN07 50KW
YB01GD02:
GN08 50KW
负荷02光伏并网箱FH02GD03
GN01 50KW
GN02 33KW
负荷02光伏并网信令箱FH02GD03R3
并网点 5
厂区次入口
负荷02光伏并网箱
FH02GD02
一层楼梯口配电室
负荷02光伏并网信令箱FH02GD02R3
GN01 50KW
宿舍楼 3F
并网点 6
635
食堂 钢结构 1F
X=155891.835
Y=122891.698
6.1

园区平面图